

וְעַל-מִזְבֵּחַ תְּמִימָה תְּמִימָה וְעַל-מִזְבֵּחַ תְּמִימָה תְּמִימָה

KIRRAN

DRIVI

SHORT LINES

- ① 189°32'15" 9.225
② 179°14' 6.15

Surveyor : IAN ROBERT SPARK
Date of Survey : 18/03/2008
Surveyor's Ref : 3908

PLAN OF SUBDIVISION OF LOT 43 OF DP 248781

LGA 2000-2001

Registered
10-8-2009

DP1142049


SURVEYING REGULATION 2006 CLAUSE 61 (2) & 35 (1)(b)

M.G.A. CO-ORDINATES			ATTRIBUTES			
MARK	EASTING	NORTHING	ZONE	CLASS	ORDER	ORIGIN
SSM 72545	393 609.053	6 377 618.790	56	B	2	SCIMS
PM 71583	393 302.585	6 377 318.000	56	B	2	SCIMS
PM 113278	393 461.737	6 377 273.571	56	C	3	SCIMS

COMBINED SEA LEVEL AND SCALE FACTOR 0.999737

SOURCE M.G.A. CO-ORDINATES ADOPTED FROM


S.C.I.M.S. AS AT 6th - MARCH - 2008

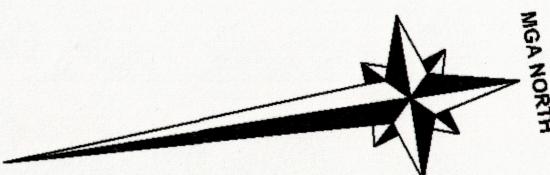

S1984/A7

- (A) EASEMENT TO DRAIN WATER 1.5 WIDE.
- (B) RESTRICTION ON THE USE OF LAND.
- (C) EASEMENT FOR SEWAGE PUMPING STATION (Z834783)

DIAGRAM 1:500

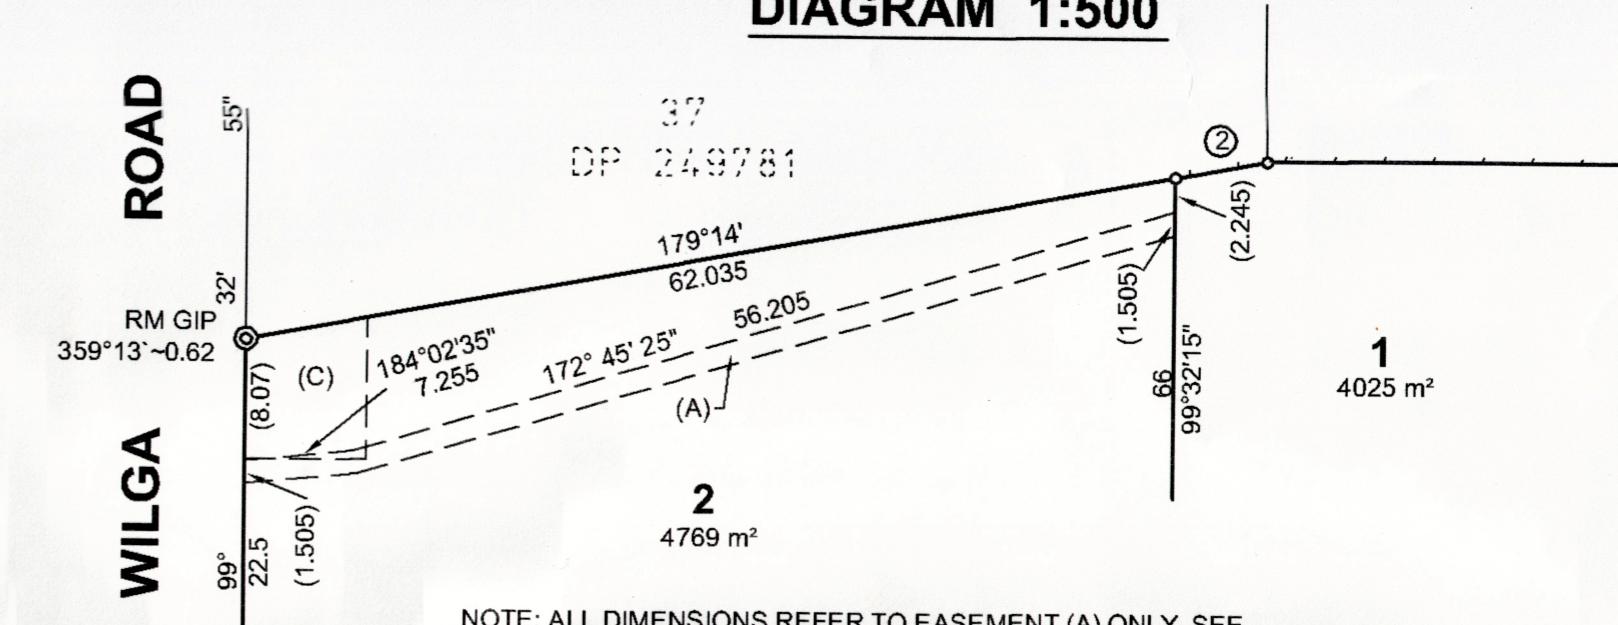

NOTE: ALL DIMENSIONS REFER TO EASEMENT (A) ONLY. SEE
DEALING Z834783 FOR DIMENSIONS OF EASEMENT (C).

DP1142049